


BOREHOLE LOG		BW-02		Demo project (synthetic)	
X / Easting:	652,150.0	Water level:	16.2 m bgl (15-02-2025)	Diameter:	165
Y / Northing:	1,688,600.0	Location:	Granite upland		
Ground elevation:	481.70 m amsl	Date:	2025-02-14		
Total depth:	80 m bgl	Drilling method:	DTH		

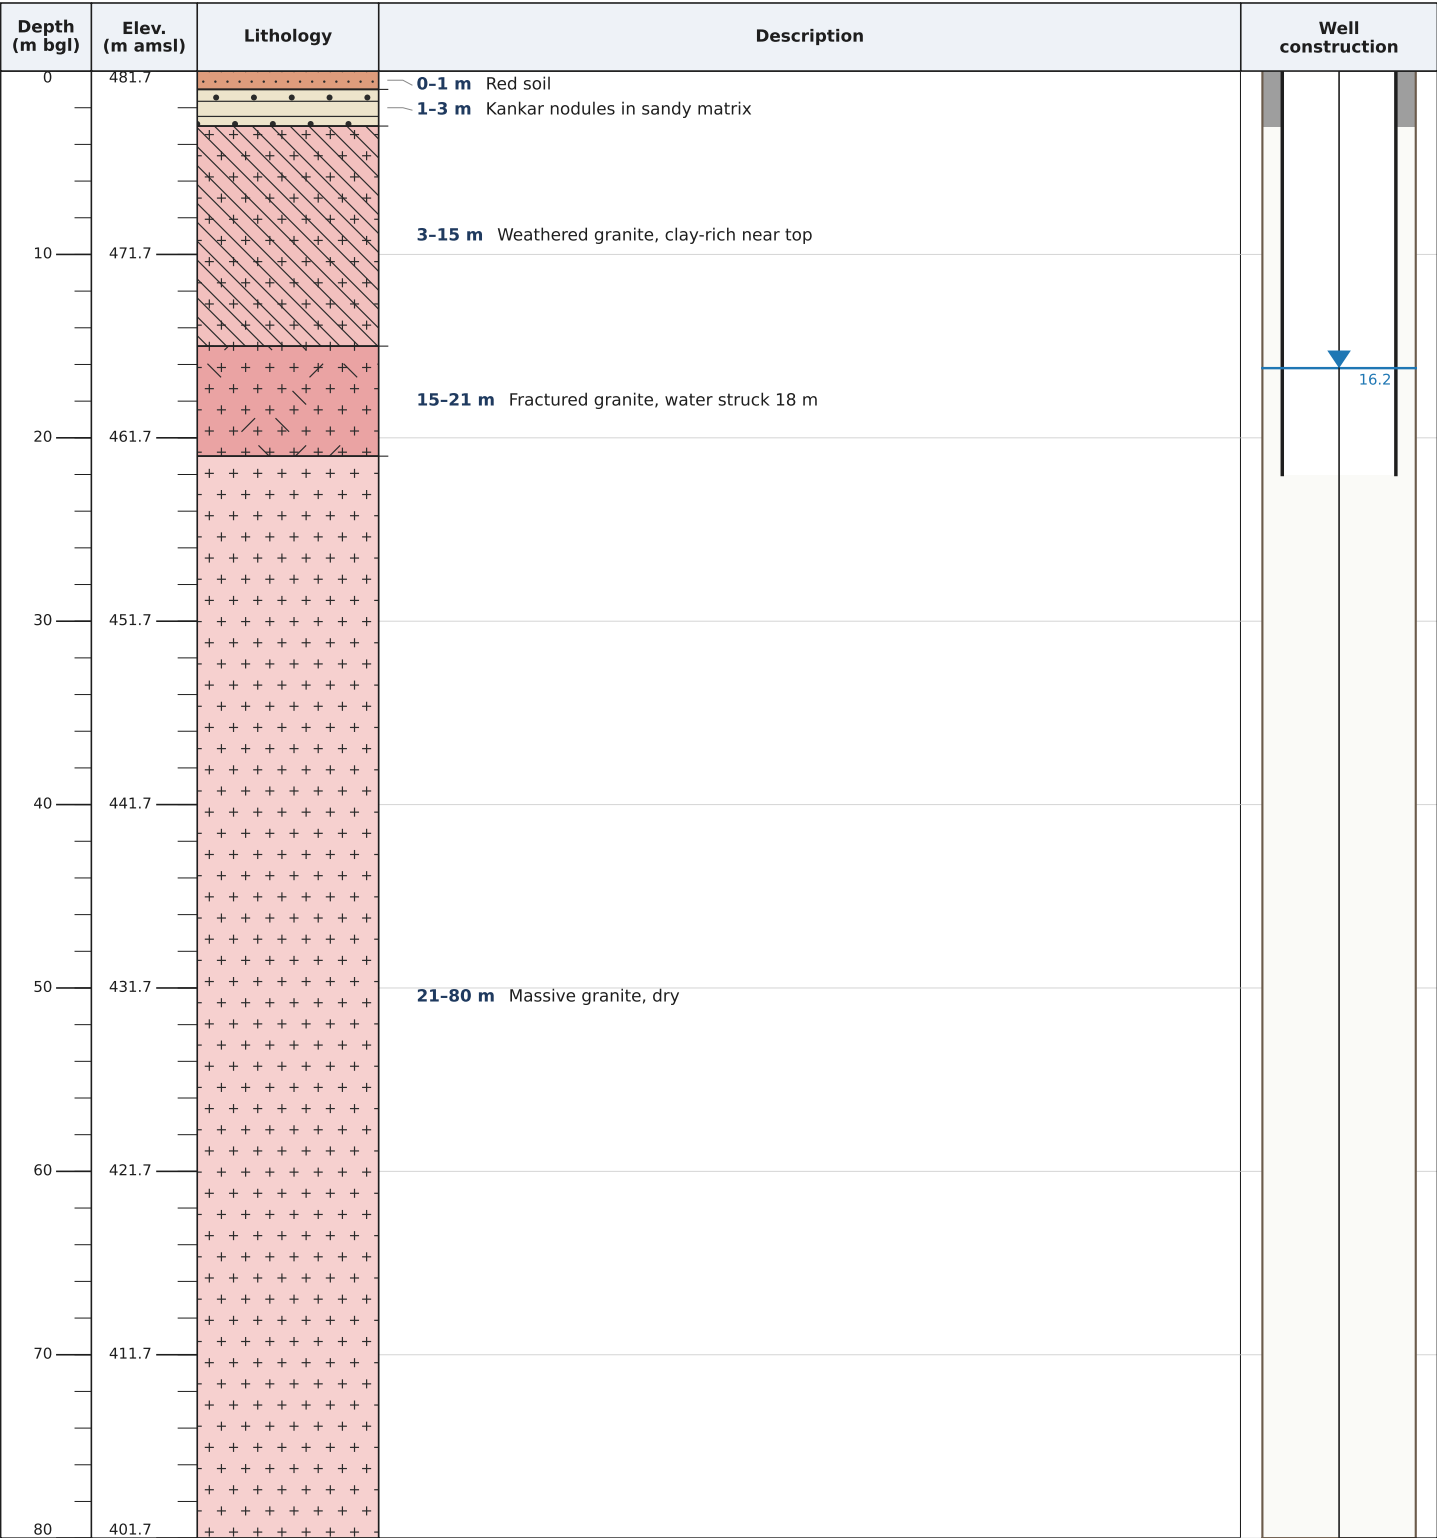

 Red soil (RSOIL)

 Granite (massive) (GRA)

 Kankar / calcrete (KANK)

 Water level (m bgl)

 Weathered granite (WGRA)

 Casing

 Fractured granite (FGRA)

 Seal / grout